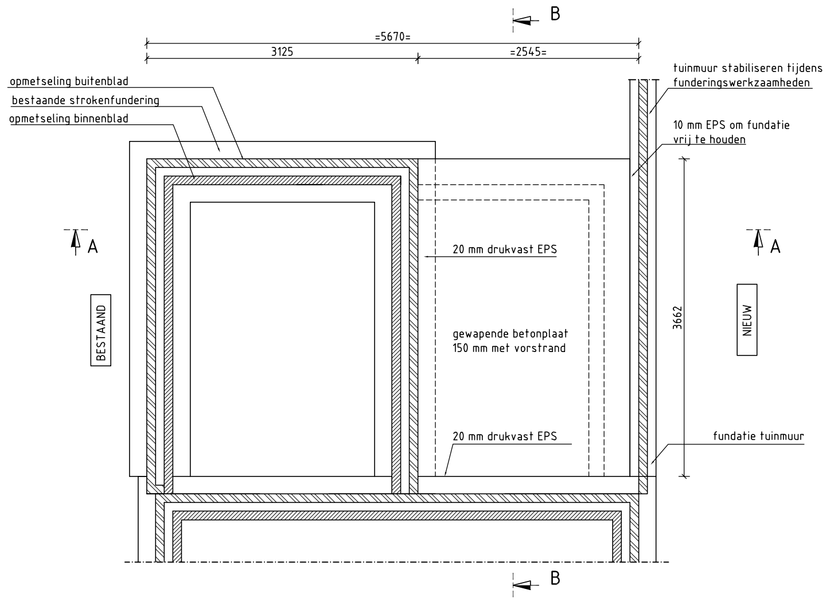
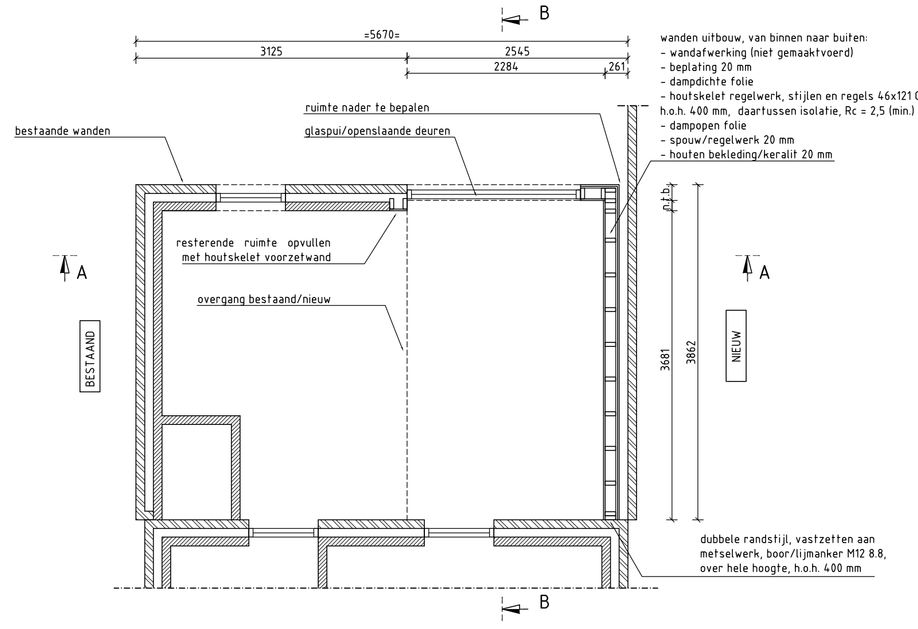


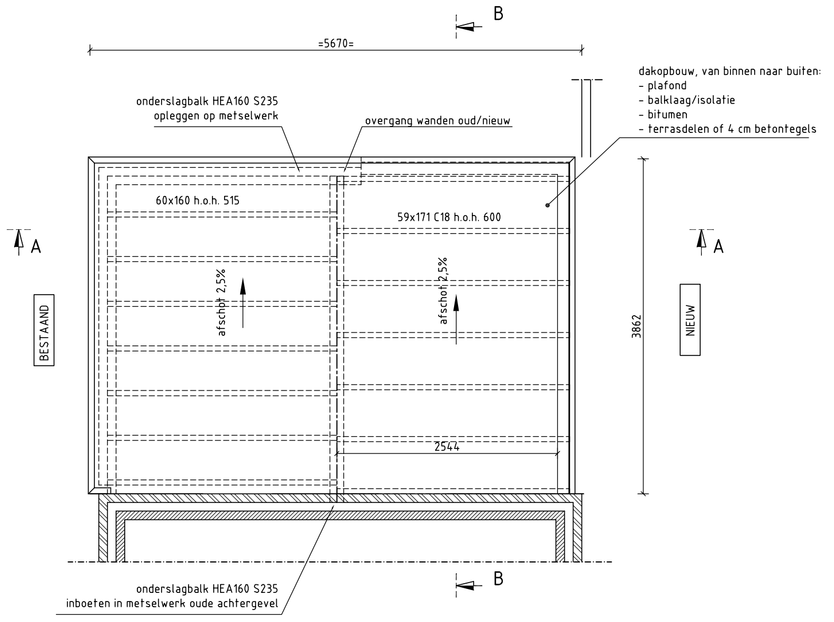

## Funderingsplan

SCHAAL 1:50



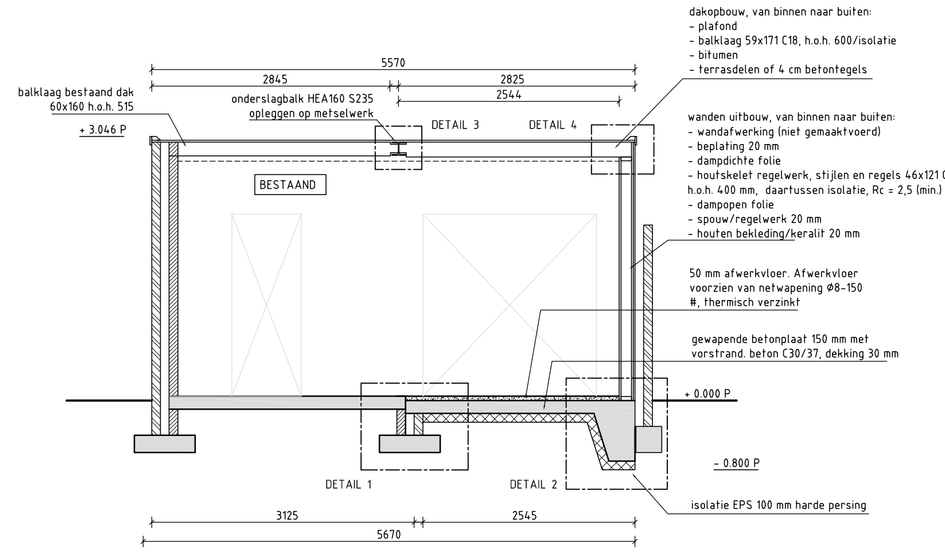

## Plattegrond begane grond

SCHAAL 1:50



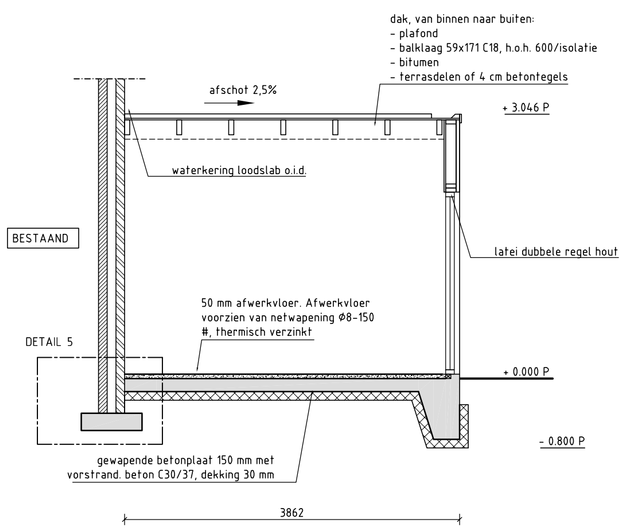

## Dakplan

SCHAAL 1:50



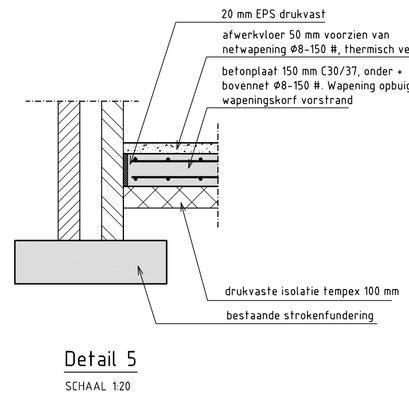

## Doorsnede A-A

SCHAAL 1:50



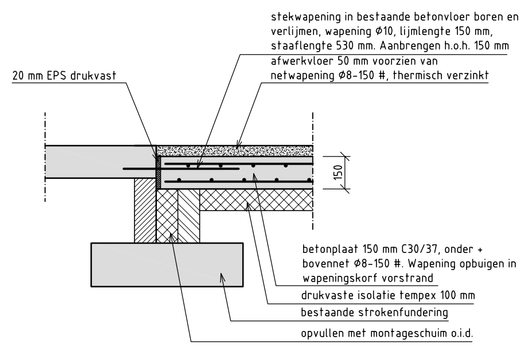

## Doorsnede B-B

SCHAAL 1:50



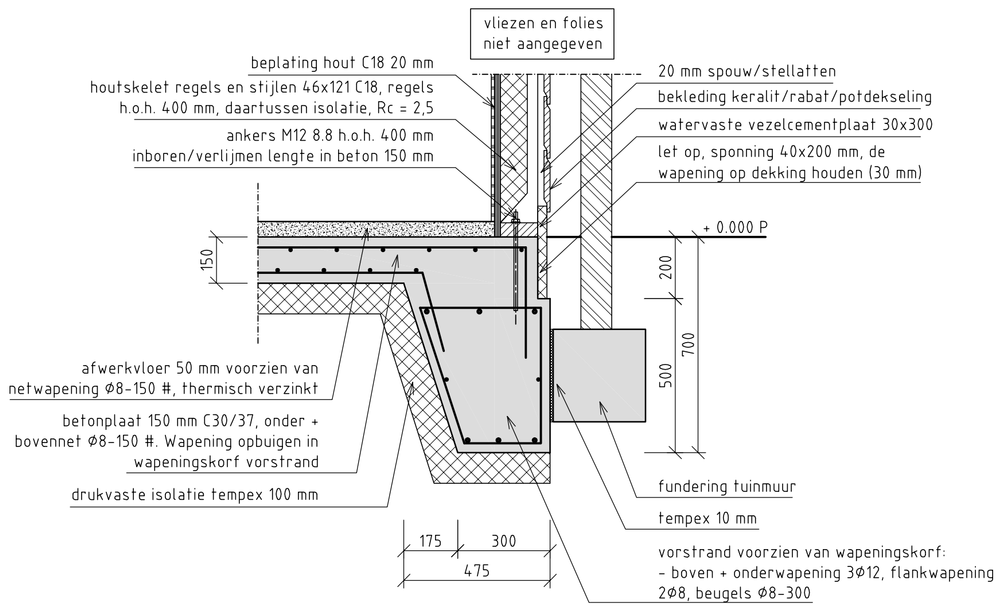

## Detail 5

SCHAAL 1:20



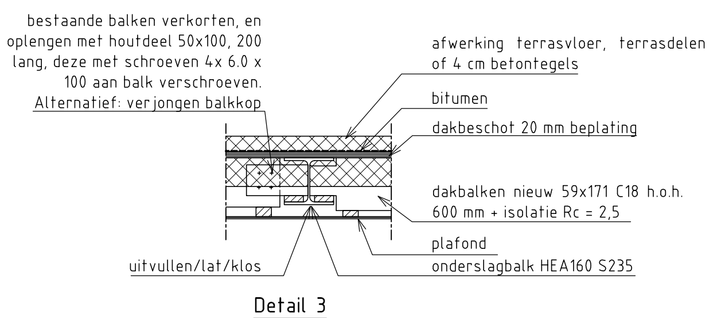

## Detail 1

SCHAAL 1:20



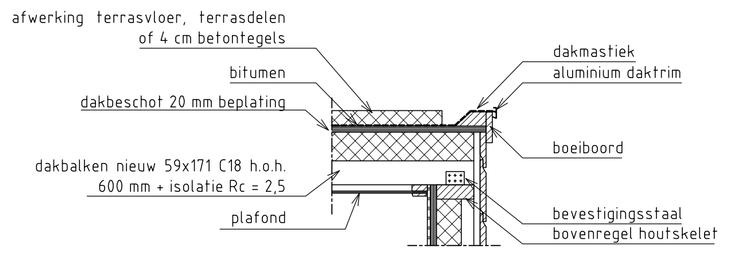

## Detail 2

SCHAAL 1:20




## Detail 3

SCHAAL 1:20




## Detail 4

SCHAAL 1:20

OPMERKINGEN / RENVOOI

- Alle maten in het werk controleren, maten aangegeven als xxx in het werk te bepalen
- Alle maten in mm, tenzij anders aangegeven

| Versie | Omschrijving |
|---|---|
| B | Enkele aanpassingen |
| A | Eerste uitgave |


WKL ENGINEERING
WILLEM DE JAGERSTRAAT 60
3251 BG STELLENDAM
t: 0643405312
e: WK-ENGINEERING@HOTMAIL.COM


# CONSTRUCTIEGEGEVENS UITBOUW KORTEWEGJE 19 SOMMELSDIJK CONSTRUCTIEVE SCHETSEN

| | | | |
|---|---|---|---|
| Opdrachtgever | Dhr. Jonker | Tekenaar | WKL |
| Werknummer | 2014-29 | Versie | B |
| Tekeningcode | TEK-01 | Status | Definitief |
| Datum | 16 september 2014 | Formaat | A1 |